
TOWER ABOVE — see the tower package

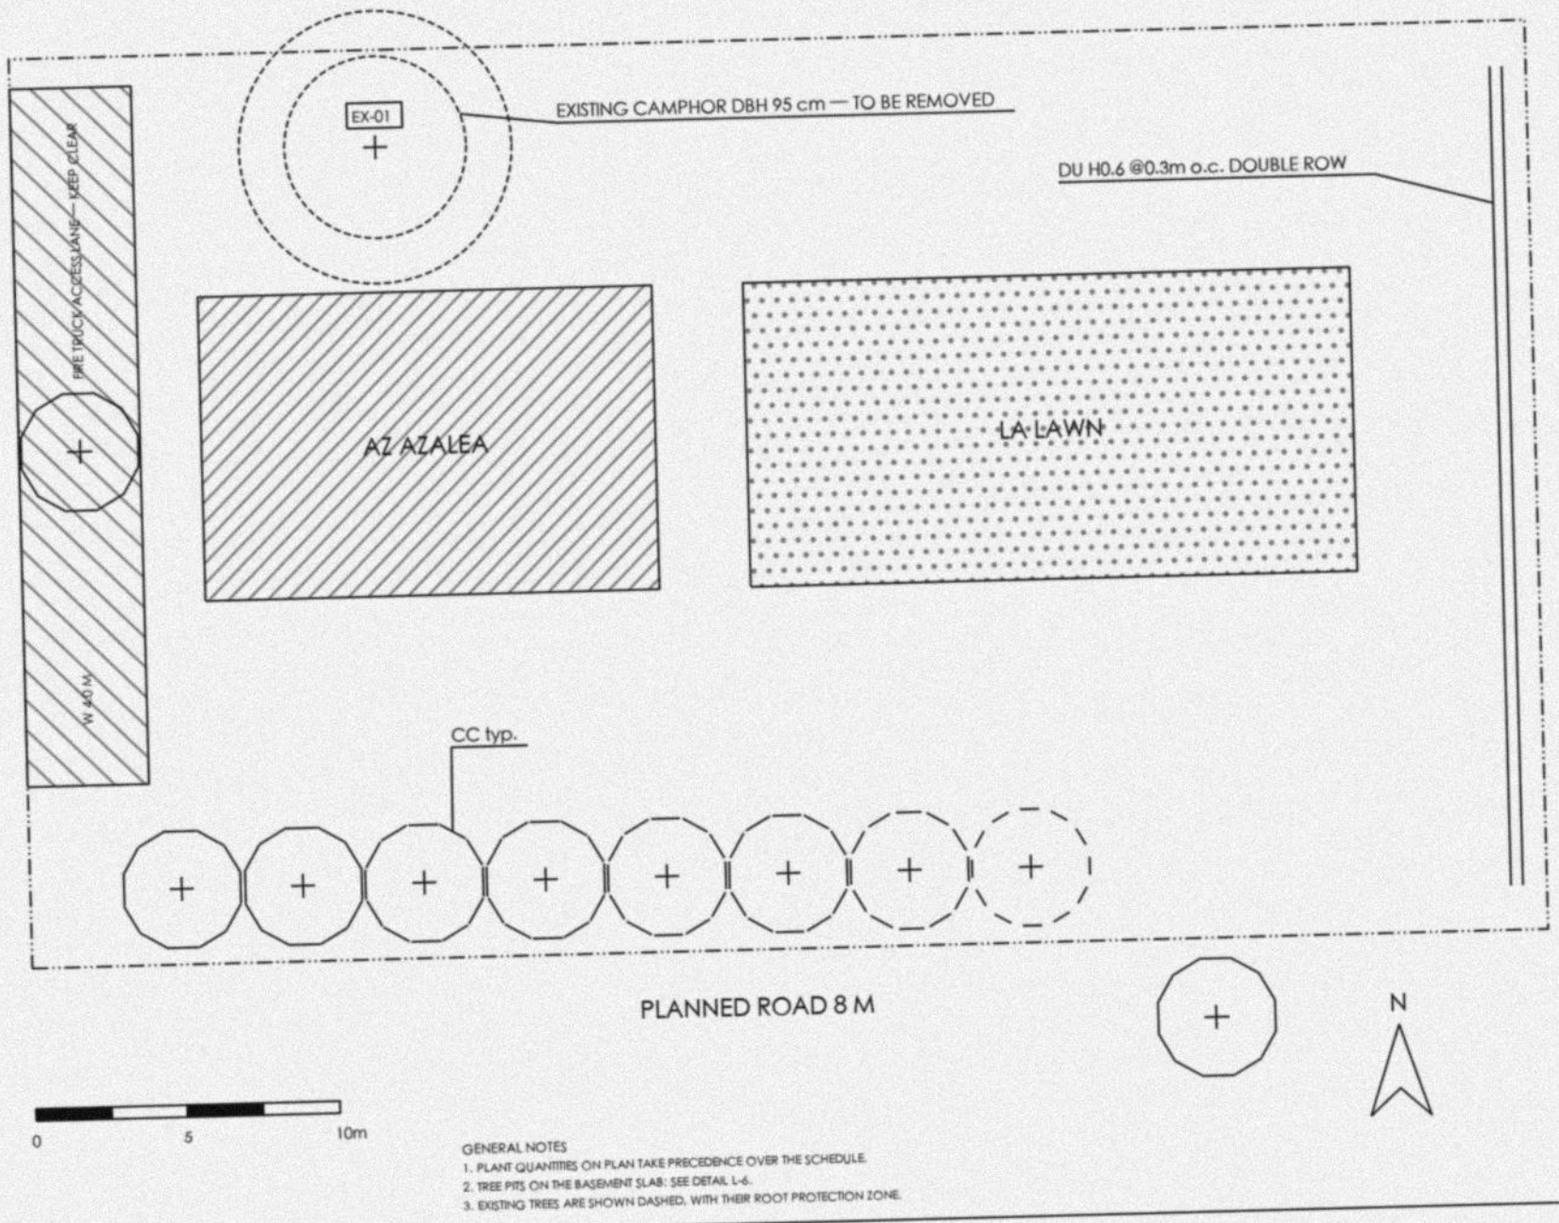

LEGEND

- CC CAMPHOR
- AZ AZALEA
- FIRE TRUCK ACCESS LANE
- DU DURANTA

PROJECT	Greenfield Residences
WORKS	Landscape over basement slab
TITLE	Planting Plan
DRAWING NO.	L-1
SCALE	1:200
SITE AREA	1,500 m²
BUILDING COVERAGE	40%
GROUND	ARTIFICIAL GROUND
REV	A
DATE	2026-09-18

REVISIONS

A	2026-09-18	ISSUED FOR REVIEW

GENERAL NOTES
1. PLANT QUANTITIES ON PLAN TAKE PRECEDENCE OVER THE SCHEDULE.
2. TREE PITS ON THE BASEMENT SLAB: SEE DETAIL L-6.
3. EXISTING TREES ARE SHOWN DASHED, WITH THEIR ROOT PROTECTION ZONE.