GREENFIELD RESIDENCES

LANDSCAPE PACKAGE

Landscape over basement slab

ISSUED FOR REVIEW · REV A · 2026-09-18

DEVELOPER: GREENFIELD DEVELOPMENT CO. (SAMPLE)

LANDSCAPE CONSULTANT: SAMPLE LANDSCAPE STUDIO


DRAWING INDEX			
SHEET NO.	TITLE	SCALE	REV
L-1	Planting Plan	1:200	A
L-2	South Elevation	1:100	A
L-3	Paving Plan	1:200	A
L-4	Plant Schedule	NTS	A
L-5	Enlarged Plan - West	1:100	A
L-6	Tree Pit Detail	1:20	A
L-7	Irrigation Plan	1:200	A
L-8	Lighting Plan	1:200	A
L-9	Sections	1:50	A

GENERAL

1. ALL DIMENSIONS IN METRES UNLESS NOTED.
2. PLANT QUANTITIES ON PLAN TAKE PRECEDENCE OVER THE SCHEDULE.
3. READ WITH THE TREE PIT STANDARD AND THE PROCUREMENT STANDARD.

PROJECT	Greenfield Residences	
WORKS	Landscape over basement slab	
TITLE	Cover and Index	
DRAWING NO.	L-0	
SCALE	NTS	
SITE AREA	1,500 m²	
BUILDING COVERAGE	40%	
GROUND	ARTIFICIAL GROUND	
REV	A	
DATE	2026-09-18	
REVISIONS		
A	2026-09-18	ISSUED FOR REVIEW

TOWER ABOVE — see the tower package

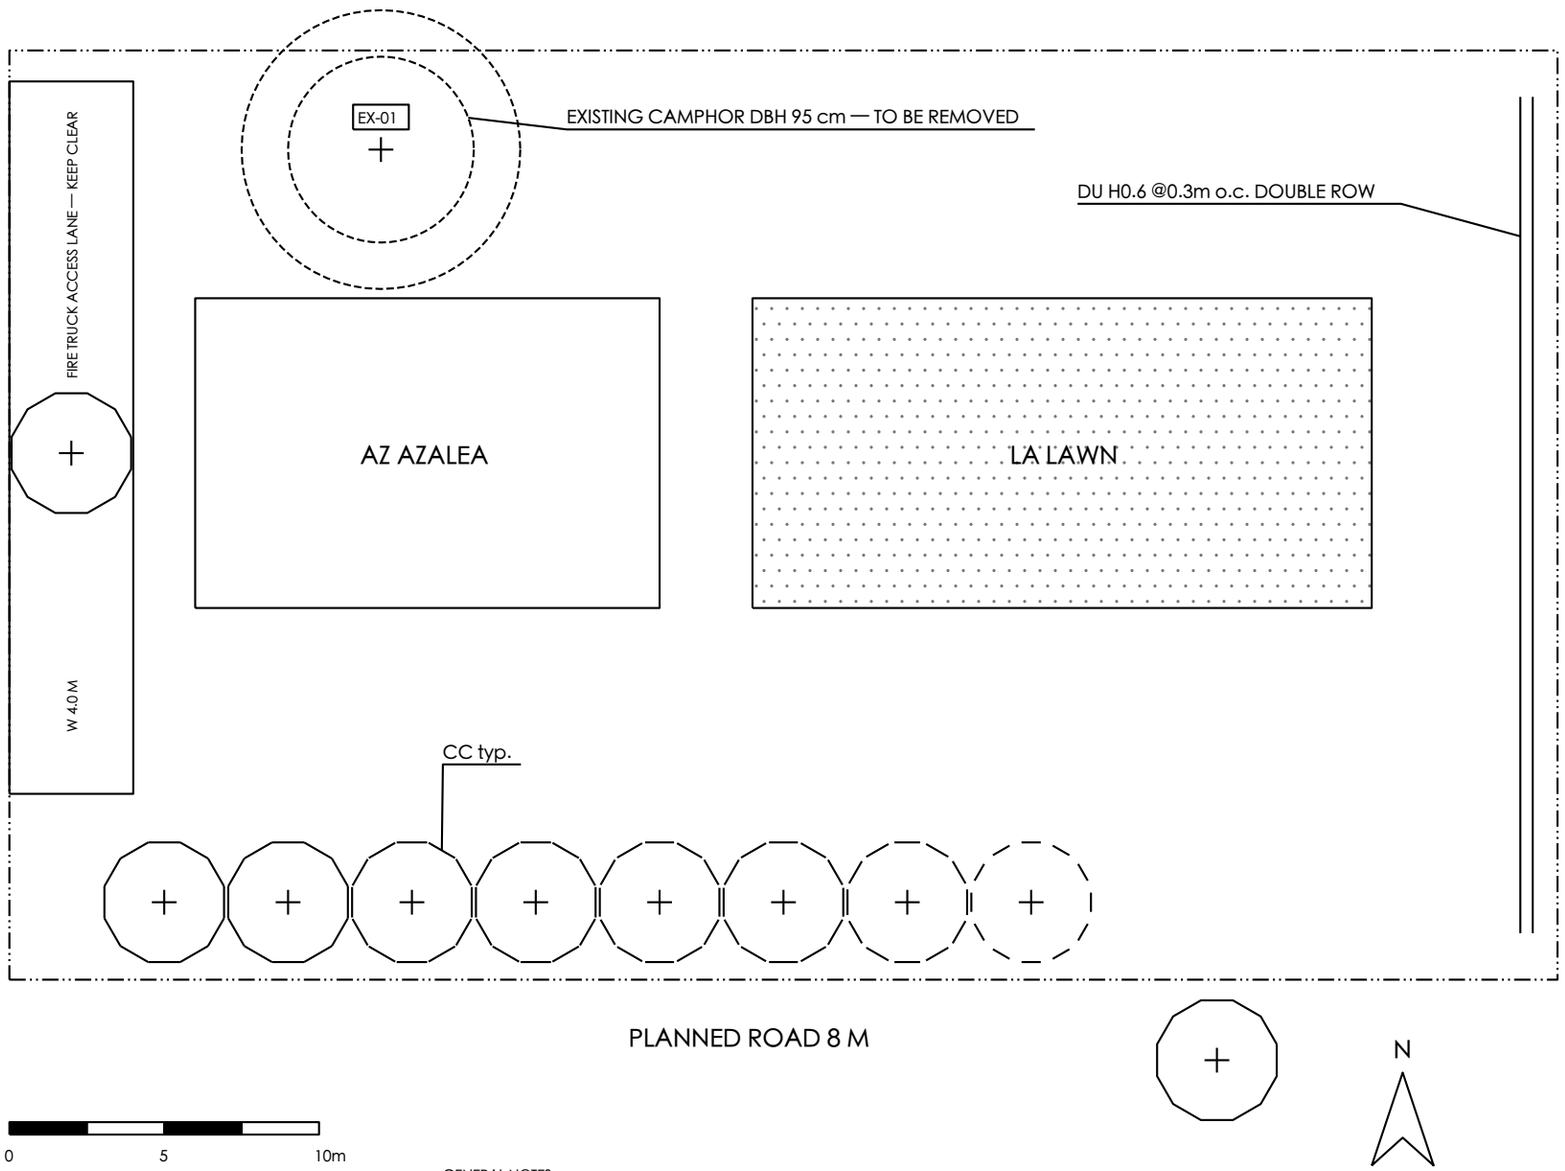

LEGEND


- CC CAMPHOR
- AZ AZALEA
- FIRE TRUCK ACCESS LANE
- DU DURANTA

PROJECT	Greenfield Residences
WORKS	Landscape over basement slab
TITLE	Planting Plan
DRAWING NO.	L-1
SCALE	1:200
SITE AREA	1,500 m²
BUILDING COVERAGE	40%
GROUND	ARTIFICIAL GROUND
REV	A
DATE	2026-09-18

REVISIONS		
A	2026-09-18	ISSUED FOR REVIEW


GENERAL NOTES

1. PLANT QUANTITIES ON PLAN TAKE PRECEDENCE OVER THE SCHEDULE.
2. TREE PITS ON THE BASEMENT SLAB: SEE DETAIL L-6.
3. EXISTING TREES ARE SHOWN DASHED, WITH THEIR ROOT PROTECTION ZONE.

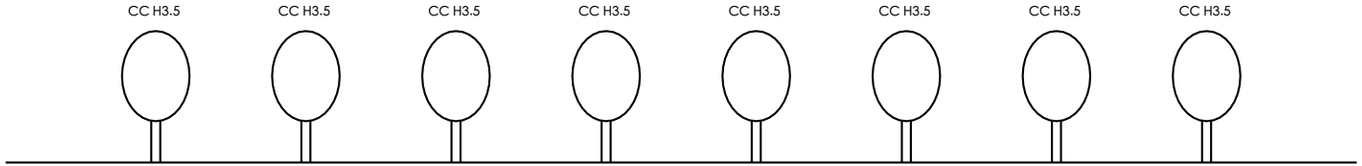

SOUTH ELEVATION 1:100

PROJECT		Greenfield Residences
WORKS		Landscape over basement slab
TITLE		South Elevation
DRAWING NO.		L-2
SCALE		1:100
SITE AREA		1,500 m²
BUILDING COVERAGE		40%
GROUND		ARTIFICIAL GROUND
REV		A
DATE		2026-09-18
REVISIONS		
A	2026-09-18	ISSUED FOR REVIEW

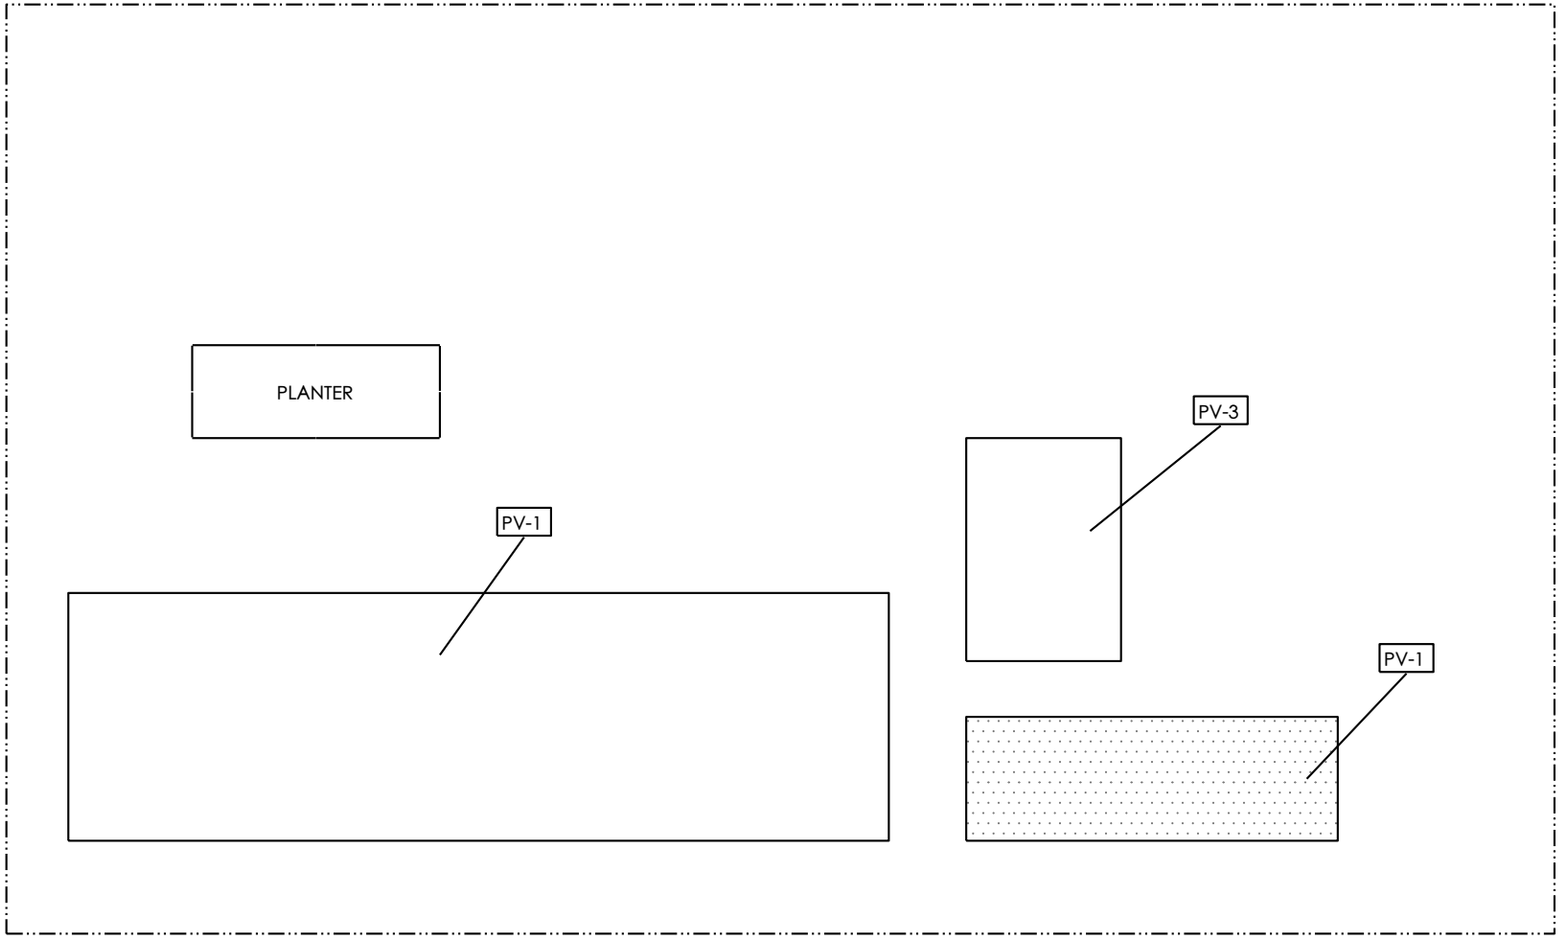

LEGEND

- PV-1 PERMEABLE PAVERS
- PV-2 EXPOSED AGGREGATE
- PV-3 GRASS PAVERS

0 5 10m

N

PROJECT	Greenfield Residences
WORKS	Landscape over basement slab
TITLE	Paving Plan
DRAWING NO.	L-3
SCALE	1:200
SITE AREA	1,500 m²
BUILDING COVERAGE	40%
GROUND	ARTIFICIAL GROUND
REV	A
DATE	2026-09-18

REVISIONS		
A	2026-09-18	ISSUED FOR REVIEW

PLANT SCHEDULE


CODE	COMMON NAME	BOTANICAL NAME	QTY	UNIT	SPEC			REMARKS
					CAL. (cm)	HT (m)	SPREAD (m)	
TREES								
CC	Camphor	Cinnamomum camphora	12	EA	10	3.5	1.5	NATIVE, ROOT-BALLED
SHRUBS								
DU	Duranta	Duranta erecta	182	EA	-	0.6	-	@0.3m o.c., DOUBLE ROW
AZ	Azalea	Rhododendron spp.	150	m²	-	0.3	-	4 PLANTS/m²
GROUNDCOVERS								
LA	Lawn	Zoysia matrella	200	m²	-	-	-	SOD
TOTAL TREES: 12								

PROJECT	Greenfield Residences
WORKS	Landscape over basement slab
TITLE	Plant Schedule
DRAWING NO.	L-4
SCALE	NTS
SITE AREA	1,500 m²
BUILDING COVERAGE	40%
GROUND	ARTIFICIAL GROUND
REV	A
DATE	2026-09-18


REVISIONS		
A	2026-09-18	ISSUED FOR REVIEW

ENLARGED PLAN — WEST

SCALE 1:100

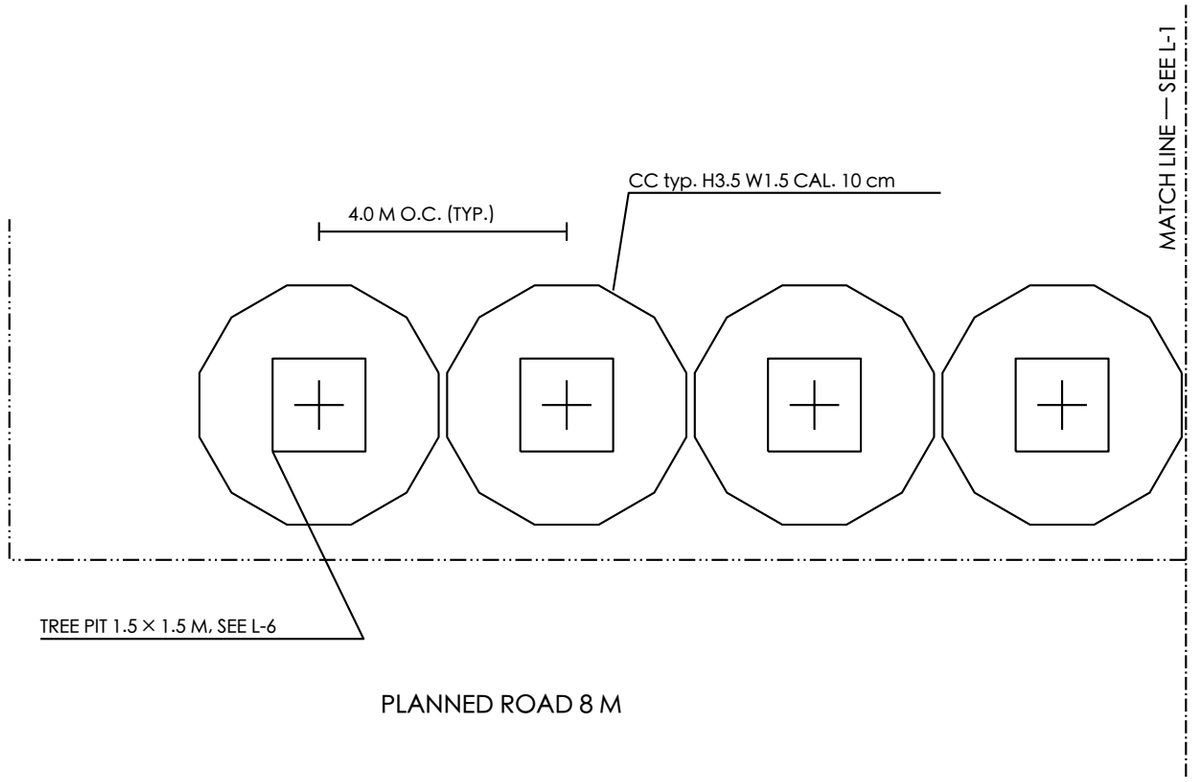

KEY PLAN

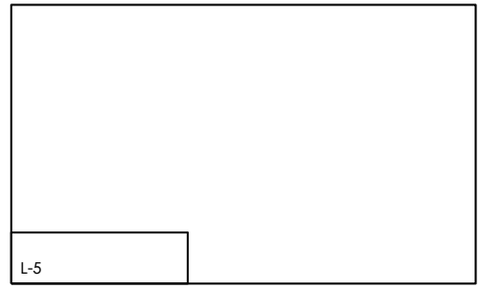






PROJECT		Greenfield Residences
WORKS		Landscape over basement slab
TITLE		Enlarged Plan - West
DRAWING NO.		L-5
SCALE		1:200
SITE AREA		1,500 m²
BUILDING COVERAGE		40%
GROUND		ARTIFICIAL GROUND
REV		A
DATE		2026-09-18
REVISIONS		
A	2026-09-18	ISSUED FOR REVIEW


TREE PIT 1500 × 1500 · SOIL DEPTH 1000 · ON SLAB

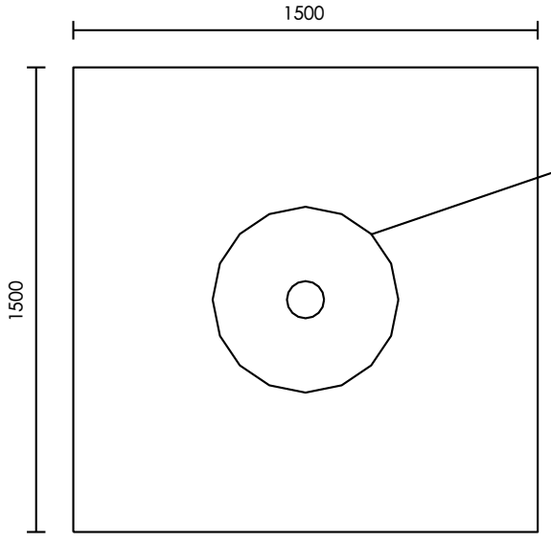

TREE PIT 1500 × 1500 · SOIL DEPTH 1000 · ON SLAB

PIT AREA 2.25 m²

PLAN 1:20

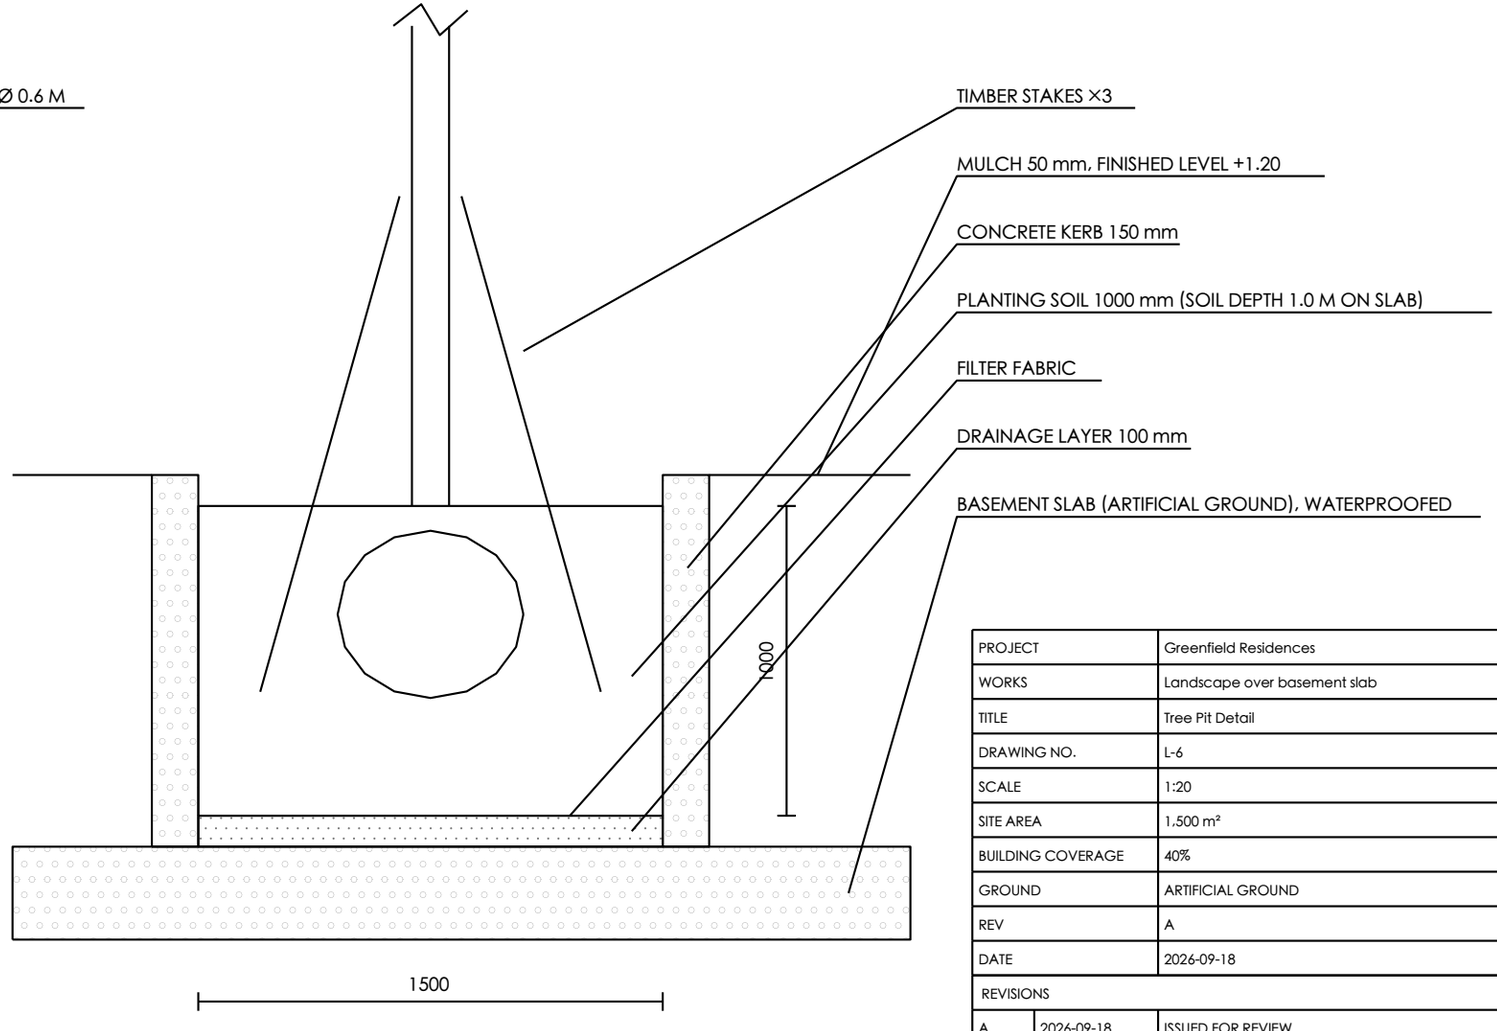


SECTION A-A 1:20

NOTES

1. PIT 1500 × 1500 = 2.25 m².
2. PLANTING SOIL 1.0 M ON THE BASEMENT SLAB.
3. FOR ALL CC CAMPHOR ON THE PODIUM (L-1).

PROJECT	Greenfield Residences
WORKS	Landscape over basement slab
TITLE	Tree Pit Detail
DRAWING NO.	L-6
SCALE	1:20
SITE AREA	1,500 m²
BUILDING COVERAGE	40%
GROUND	ARTIFICIAL GROUND
REV	A
DATE	2026-09-18


REVISIONS		
A	2026-09-18	ISSUED FOR REVIEW

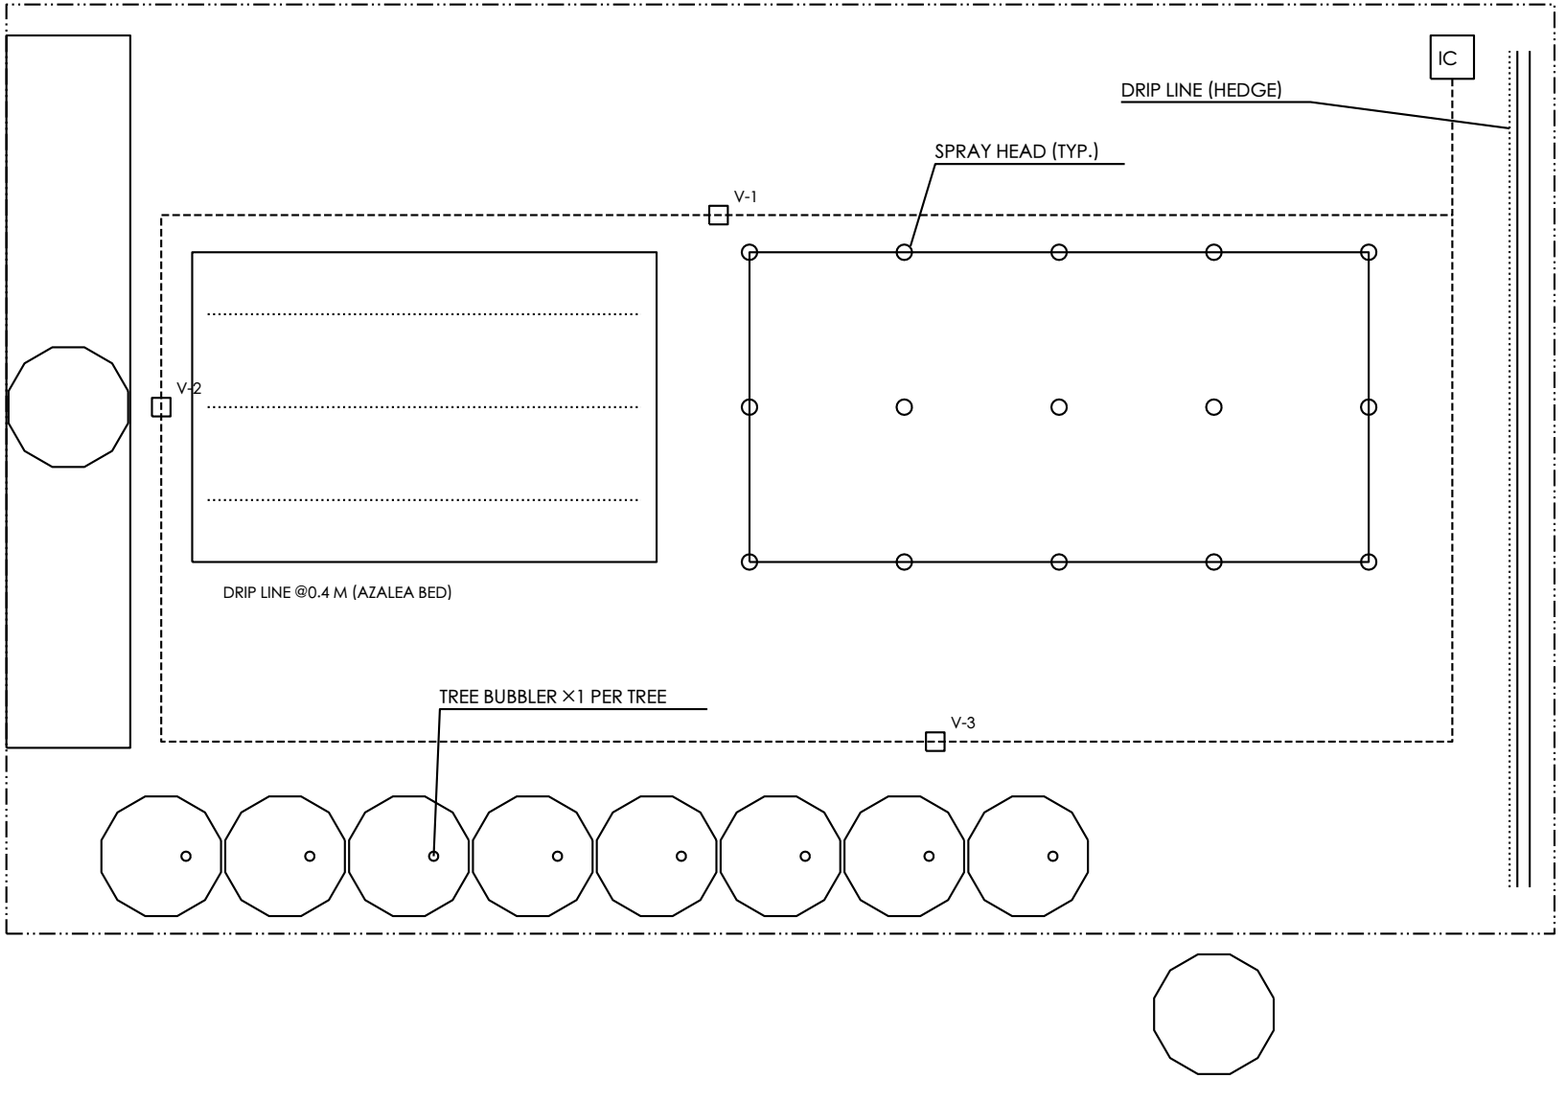

IRRIGATION LEGEND

○	SPRAY HEAD, POP-UP
□	SOLENOID VALVE
○	TREE BUBBLER
------	PE MAINLINE 32 mm
.....	DRIP LINE 16 mm

PROJECT		Greenfield Residences
WORKS		Landscape over basement slab
TITLE		Irrigation Plan
DRAWING NO.		L-7
SCALE		1:200
SITE AREA		1,500 m²
BUILDING COVERAGE		40%
GROUND		ARTIFICIAL GROUND
REV		A
DATE		2026-09-18
REVISIONS		
A	2026-09-18	ISSUED FOR REVIEW

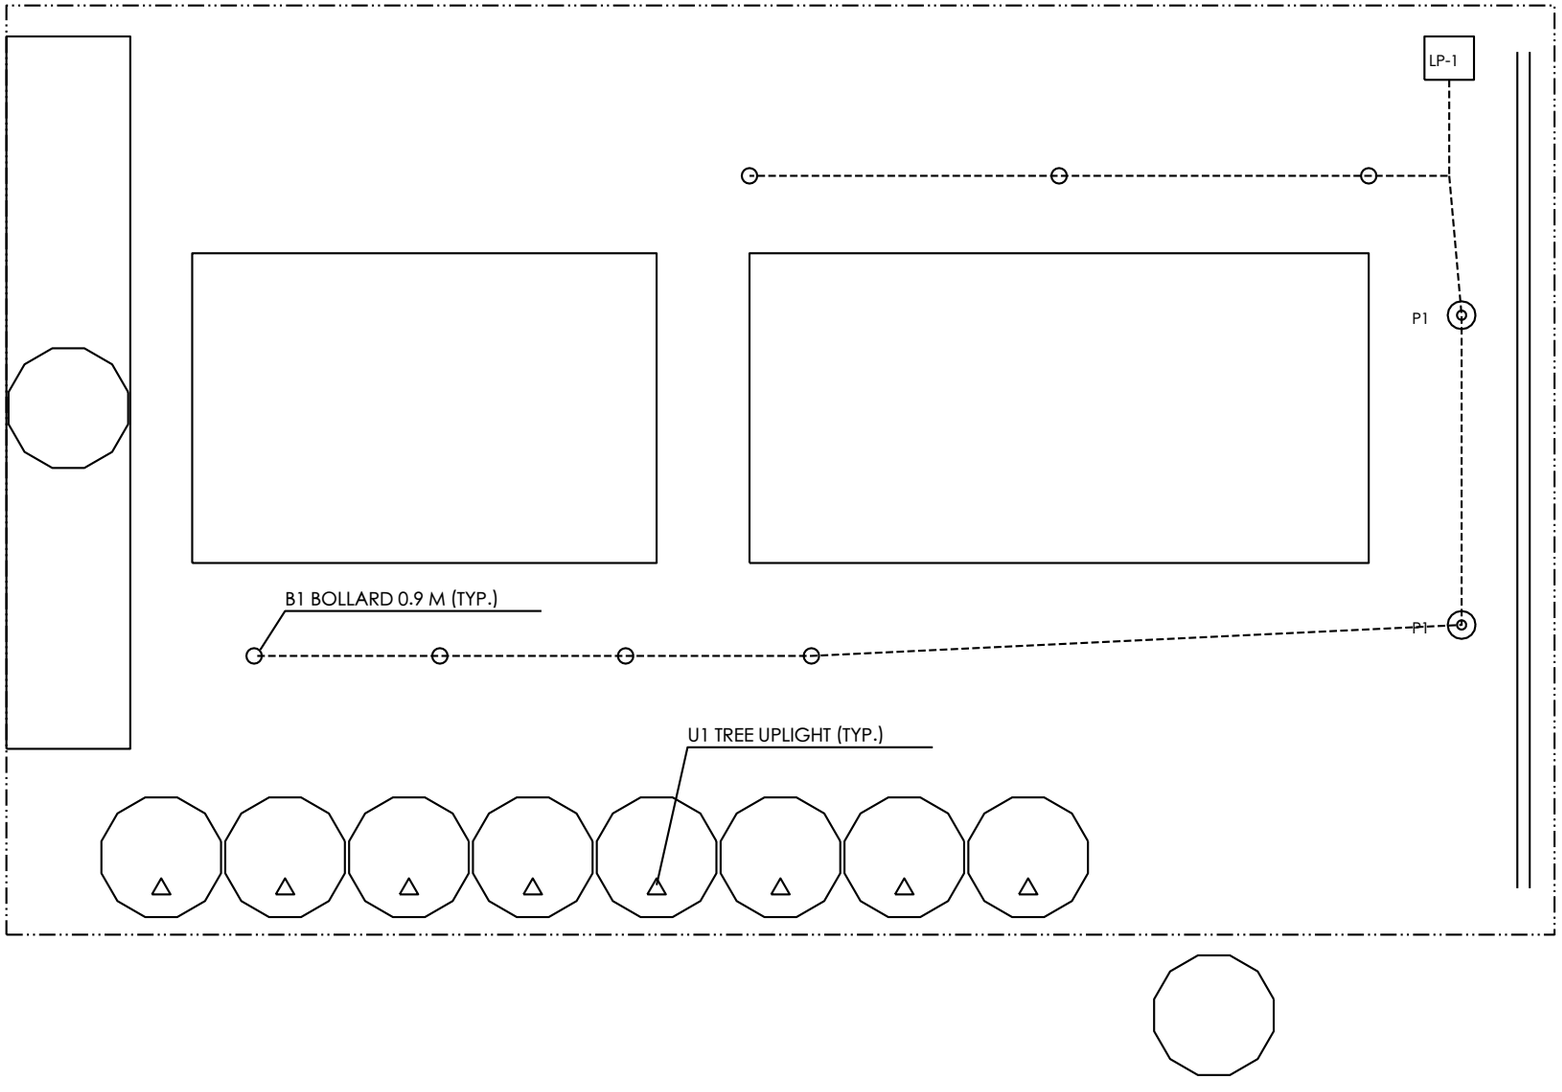

LIGHTING LEGEND

○	B1 BOLLARD
△	U1 TREE UPLIGHT
◎	P1 POLE LIGHT 4 M
------	CIRCUIT

PROJECT		Greenfield Residences
WORKS		Landscape over basement slab
TITLE		Lighting Plan
DRAWING NO.		L-8
SCALE		1:200
SITE AREA		1,500 m²
BUILDING COVERAGE		40%
GROUND		ARTIFICIAL GROUND
REV		A
DATE		2026-09-18
REVISIONS		
A	2026-09-18	ISSUED FOR REVIEW